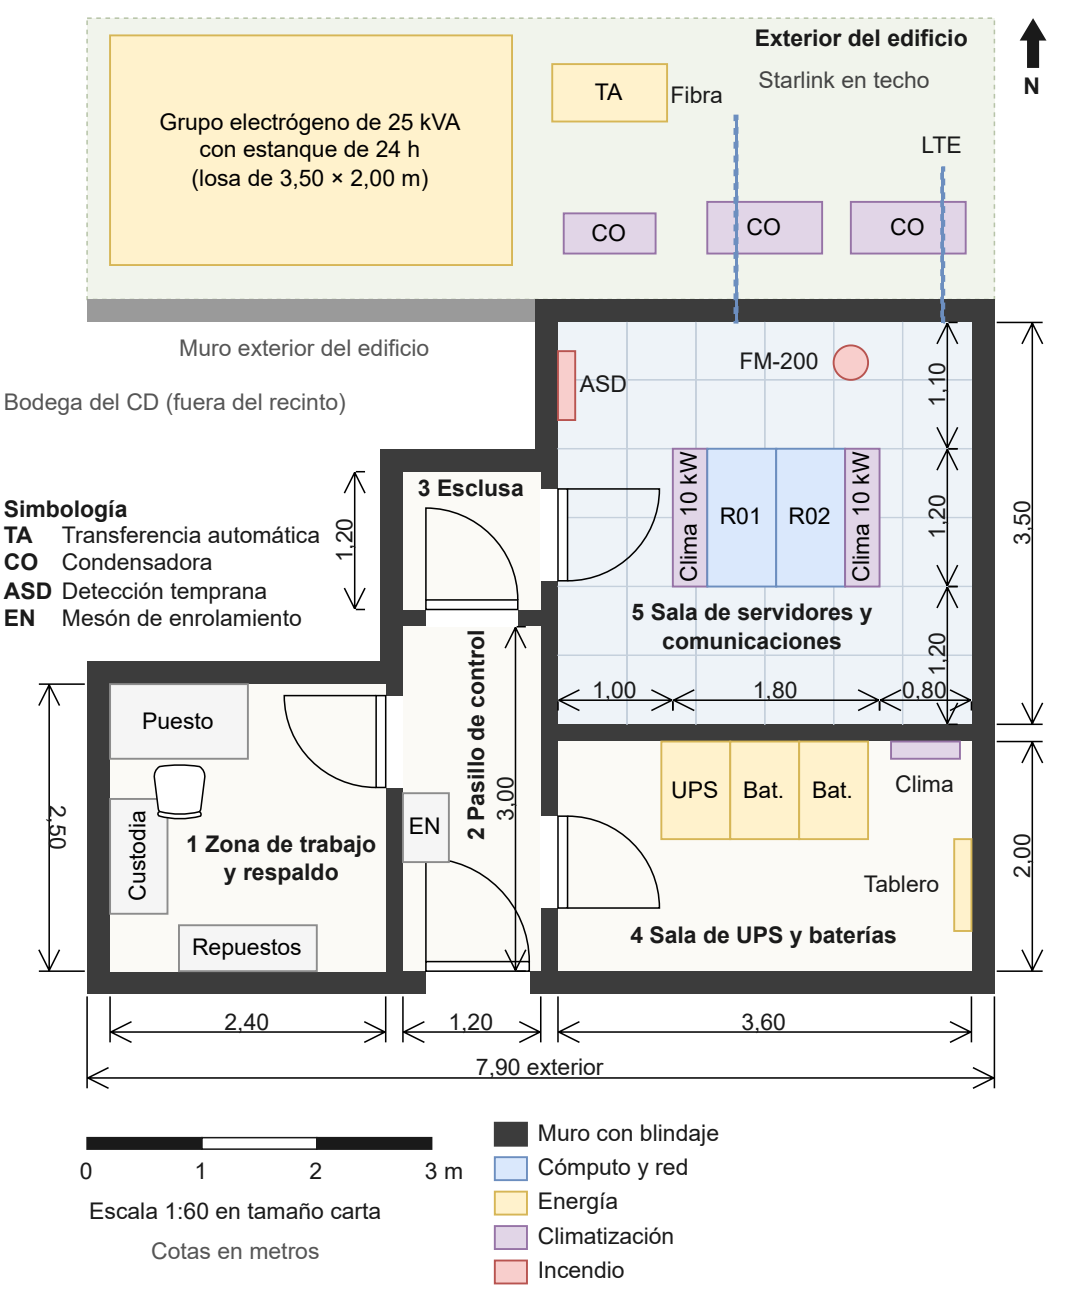

Exterior del edificio
N
Grupo electrógeno de 25 kVA
con estanque de 24 h
(losa de 3,50 × 2,00 m)
TA
Fibra
Starlink en techo
LTE
CO
CO
CO
Muro exterior del edificio
Bodega del CD (fuera del recinto)
ASD
FM-200
1,10
1,20
1,20
3,50
Clima 10 kW
R01
R02
Clima 10 kW
3 Esclusa
1,20
5 Sala de servidores y
comunicaciones
1,00
1,80
0,80
Simbología
TA Transferencia automática
CO Condensadora
ASD Detección temprana
EN Mesón de enrolamiento
Puesto
2 Pasillo de control
3,00
UPS
Bat.
Bat.
Clima
2,50
Custodia
1 Zona de trabajo
y respaldo
EN
Tablero
2,00
Repuestos
4 Sala de UPS y baterías
2,40
1,20
3,60
7,90 exterior
0
1
2
3 m
Escala 1:60 en tamaño carta
Cotas en metros
Muro con blindaje
Cómputo y red
Energía
Climatización
Incendio